ОЛИМПРОЕКТ
Архитектура. Изыскания. Проектирование.

ОБЩЕСТВО С ОГРАНИЧЕННОЙ ОТВЕТСТВЕННОСТЬЮ

«ГРУППА КОМПАНИЙ «ОЛИМПРОЕКТ»

РАБОЧАЯ ДОКУМЕНТАЦИЯ

Лестничные клетки. Ограждения лестничных клеток

133/23-ГК-АР6

ОБЪЕКТ: Жилой комплекс, расположенный по адресу: г. Москва, Мосфильмовская ул., вл. 31А

ЗАКАЗЧИК: ООО "СЗ "ОКТЯБРЬ-ДЕВЕЛОПМЕНТ"

Изм	№ док	Подп.	Дата
1	2032/25		15.07.25

Москва, 2024 г.

ОЛИМПРОЕКТ
Архитектура. Изыскания. Проектирование.

ОБЩЕСТВО С ОГРАНИЧЕННОЙ ОТВЕТСТВЕННОСТЬЮ

«ГРУППА КОМПАНИЙ «ОЛИМПРОЕКТ»

РАБОЧАЯ ДОКУМЕНТАЦИЯ

Лестничные клетки. Ограждения лестничных клеток

133/23-ГК-АР6

ОБЪЕКТ:	Жилой комплекс, расположенный по адресу: г. Москва, Мосфильмовская ул., вл. 31А
ЗАКАЗЧИК:	ООО "СЗ "ОКТЯБРЬ-ДЕВЕЛОПМЕНТ"

Генеральный директор	Н.Ю. Сухих
Заместитель директора БКП по архитектурным решениям	Т.С. Локтева
Главный инженер проектов	А.Н. Якубовский

Москва, 2024 г.

Разрешение	Обозначение	133/23-ГК-АР6
2032/25	Наименование объекта строительства	«Жилой комплекс, расположенный по адресу: г. Москва, Мосфильмовская ул., вл. 31А», расположенный по адресу: г. Москва, Мосфильмовская ул., вл. 31А

Изм.	Лист	Содержание изменения	Код	Примечание
1.1	1	Внесены изм. в ведомость рабочих чертежей основного комплекта 133/23-ГК-АР6, ведомость спецификаций комплекта 133/23-ГК-АР6	1	
Зам	2	Изменена конфигурация наружной лестницы строения №1, уточнена спецификация элементов фасада, уточнена сводная ведомость материалов	1	
Зам	3	Корректировка типа ограждений лестничной клетки в соответствии с решениями АИ, корректировка ЛК и ограждений в отметках +51.150 - +55.350	1	
Зам	4	Уточнение эскизов ограждений, уточнение спецификации элементов ограждений НЧ, уточнение ведомости ограждений лестниц, уточнение схем крепления ограждений и поручней	1	

Согласовано:

Н. Контр.

Изм. внес	Алексеева		07.2025
Составил	Алексеева		07.2025
ГИП	Якубовский		07.2025
Утв.	Локтева		07.2025

ОЛИМПРОЕКТ
Архитектура. Изыскания. Проектирование.

Лист	Листов
1	2

Ведомость ссылочных и прилагаемых документов

Обозначение	Наименование	Примечание
Федеральный закон от 22.07.2008 г (с изм от 25.12.2023)№123-ФЗ	Технический регламент о требованиях пожарной безопасности	
Федеральный закон от 27.12.2002 (с изм. от 02.07.2021) N 184-ФЗ	О техническом регулировании	
Федеральный закон от 29.12.2004 (с изм. 25.12.2023) №190-ФЗ	Градостроительный кодекс Российской Федерации	
Федеральный закон от 30.12.2009 (с изм. 02.07.2013) N 384-ФЗ	Технический регламент о безопасности зданий и сооружений	
СП 1.13130.2020 (с Изменением N1 от 21.11.2023)	Системы противопожарной защиты. Эвакуационные пути и выходы	
СП 2.13130.2020 (с Изменением N1 от 20.06.2023)	Системы противопожарной защиты. Обеспечение огнестойкости объектов защиты	
СП 1.13130.2020(с Изменением N1 от 21.11.2023)	Системы противопожарной защиты. Эвакуационные пути и выходы	
СП 3.13130.2009	Системы противопожарной защиты. Система оповещения и управления эвакуацией людей при пожаре. Требования пожарной безопасности	
СП 4.13130.2013	Системы противопожарной защиты. Ограничения распространения пожара на объектах защиты. Требования к объемно-планировочным и конструктивным решениям	
СП 7.13130.2013 (с Изменениями N1,2 от 12.03.2020)	Отопление,вентиляция и кондиционирование. Требования пожарной безопасности	
СП 8.13130.2020	Системы противопожарной защиты.Наружное противопожарное водоснабжение.Требования пожарной безопасности	
СП 10.13130.2020	Системы противопожарной защиты.Внутренний противопожарный водопровод.Требования пожарной безопасности	
СП 15.13330.2020 (с Изменением N1 от 21.12.2023)	Каменные и армокаменные конструкции	
СП 17.13330.2017	Кровли. Актуализированная редакция СНиП 11-26-76 (с изменением №1)	
СП 29.13330.2011	Полы	
СП 54.13330.2022	Здания жилые многоквартирные	
СП 59.13330.2020 (с Изменениями N1,2 от 21.11.2023)	Доступность зданий и сооружений для маломобильных групп населения. Актуализированная редакция СНиП 35-01-2001	
СП 70.13330.2012 (с Изменениями N1,3-6 от 11.12.2023)	Несущие и ограждающие конструкции	
СП 118.13330.2022 (с Изменениями N1,2,3 от 25.10.2023)	Общественные здания и сооружения	
СП 160.1325800.2014 (с Изменениями №1,2,3 от 28.12.2023)	Здания и комплексы многофункциональные. Правила проектирования	
СП 477.1325800.2020	Здания и комплексы высотные.Требования пожарной безопасности	
СП 484.1311500.2020	Системы противопожарной сигнализации и автоматизация систем противопожарной защиты	
ГОСТ 31173-2016	Блоки дверные стальные. Технические условия	
ГОСТ Р 57327-2016	Двери металлические противопожарные. Общие технические требования и методы испытаний	
ГОСТ 530-2012	Кирпич и камень керамические. Общие технические условия	
ГОСТ 31360-2024	Изделия для каменной кладки. Блоки из ячеистого бетона автоклавного твердения. Технические условия	
ГОСТ 17177-94	Материалы и изделия строительные теплоизоляционные. Методы испытаний	
ГОСТ 21.501-2018	Система проектной документации для строительства (СПДС). Правила выполнения рабочей документации архитектурных и конструктивных решений	
ГОСТ 25772-2021 (с Поправками от 01.07.2023)	Ограждения металлических лестниц, балконов, крыш, лестничных маршей и площадок. Общие технические условия.	
ГОСТ Р 21.101-2020 (с Поправкой от 29.11.2023)	Система проектной документации для строительства(СПДС). Основные требования к проектной и рабочей документации	
ГОСТ 21.201-2011	Система проектной документации для строительства. Условные графические изображения элементов зданий, сооружений и конструкций	
ГОСТ 9573-2012	Плиты из минеральной ваты на синтетическом связующем теплоизоляционные. Технические условия	
ГОСТ 8509-93	Уголки стальные горячекатаные равнополочные. Сортамент	
ГОСТ 103-2006	Прокат сортовой стальной горячекатаный полосовой. Сортамент	
ГОСТ 6465-2023	Эмали ПФ-115. Технические условия	
ГОСТ 25129-2020	Грунтовка ГФ-021. Технические условия	
ГОСТ Р 52544-2006	Прокат арматурный свариваемый периодического профиля классов А500С и В500С для армирования железобетонных конструкций	

Технические решения, принятые в рабочей документации на строительство объекта "Жилой комплекс, расположенный по адресу: г. Москва, Мосфильмовская ул., вл. 31А", соответствуют заданию на проектирование, выданным техническим условиям, требованиям действующих на территории Российской Федерации технических регламентов, стандартов, норм, сводов правил и других документов, содержащих установленные требования, и обеспечивают безопасную для жизни и здоровья людей эксплуатацию объекта при соблюдении предусмотренных в рабочей документации мероприятий.

Главный инженер проекта Якубовский А.

Ведомость основных комплектов рабочих чертежей

№ Листа	Наименование	Примечание
133/23-ГК-АР1	Маркировочные планы подземной части	
133/23-ГК-АР2	Кладочные планы подземной части	
133/23-ГК-АР3	Маркировочные планы надземной части	
133/23-ГК-АР4	Кладочные планы надземной части	
133/23-ГК-АР5	Планы кровли. Узлы, сечения. Спецификация	
133/23-ГК-АР6	Лестничные клетки. Ограждения лестничных клеток	
133/23-ГК-АР7	Узлы, сечения к планам	
133/23-ГК-АР8	Фасады. Узлы облицовки, крыльца, ограждения. Спецификация материалов и изделий	
133/23-ГК-АР9	Витражи наружные, окна. Узлы, сечения. Спецификация материалов и изделий	
133/23-ГК-АИ1	Архитектурные решения интерьеров МОП	
133/23-ГК-АИ2	Архитектурные решения интерьеров паркинга	
133/23-ГК-АИ3	Архитектурные решения интерьеров Павильон №1	
133/23-ГК-АИ4	Архитектурные решения интерьеров Павильон №2	

1.1

Ведомость рабочих чертежей основного комплекта 133/23-ГК-АР6

№ Листа	Наименование	Примечание
1	Общие данные	
2	Лестница Л-7	Изм.1(Зам.)
3	Лестничная клетка Л-1. Надземная часть.	Изм.1(Зам.)
4	Ограждения	Изм.1(Зам.)

Ведомость спецификаций комплекта 133/23-ГК-АР6

№ Листа	Наименование	Примечание
2	Сводная ведомость материалов раздела 133/23-ГК-АР6 Спецификация элементов фасада. Строение 1. Лестница	Изм.1(Зам.)
4	Ведомость ограждений лестниц Спецификация элементов ограждений НЧ	Изм.1(Зам.)

Общие характеристики проектируемого объекта

1. Рабочая документация на строительство объекта «Жилой комплекс по адресу: г. Москва, Мосфильмовская ул., вл. 31А, размещаемый на земельном участке, кадастровый №77:07:0010004:24 (адресный ориентир: г. Москва, Мосфильмовская ул., вл. 31А)» разработана на основании:
- Архитектурной концепции компании NIKKEN SEKKEI LTD;
- Договора на разработку проектной документации №133/23-ГК;
- Задания на разработку проектной и рабочей документации, утвержденного Заказчиком;

Градостроительного плана земельного участка № РФ--77-4-53-3-25-2023-3232 от 01.06.2023, подготовленного Комитетом по архитектуре и градостроительству города Москвы;
- Специальных технических условий на проектирование и строительство, в части обеспечения пожарной безопасности объекта: «Жилой комплекс по адресу: г. Москва, Мосфильмовская ул., вл. 31А, размещаемый на земельном участке, кадастровый № 77:07:0010004:24 (адресный ориентир: г. Москва, Мосфильмовская ул., вл. 31А)»;
- Специальных технических условий на проектирование и строительство объекта: «Жилой комплекс по адресу: г. Москва, Мосфильмовская ул., вл. 31А, размещаемый на земельном участке, кадастровый №77:07:0010004:24 (адресный ориентир: г. Москва, Мосфильмовская ул., вл. 31А)»;

При разработке проектной документации учтены требования следующих нормативных документов:
- Постановление Правительства РФ от 16 февраля 2008 года №87 «О составе разделов проектной документации и требованиях к их содержанию (с учетом изменений, внесенных по Постановлению Правительства РФ от 27 мая 2022 года №963)»;
- Постановление Правительства РФ № 815 от 28 мая 2021 г. Об утверждении перечня национальных стандартов и сводов правил (частей таких стандартов и сводов правил), в результате применения которых на обязательной основе обеспечивается соблюдение требований федерального закона «Технический регламент о безопасности зданий и сооружений» (с учетом изменений, внесенных по Постановлению Правительства РФ от 20 мая 2022 года №914)»;- №384-ФЗ «Технический регламент о безопасности зданий и сооружений с изменениями на 2 июля 2013 г.»;
-СП 15.13330.2020 Каменные и армокаменные конструкции;
-СП 70.13330.2012 Несущие и ограждающие конструкции;
-ГОСТ 30971-2012 Швы монтажные узлов примыкания оконных блоков к стеновым проемам;
-СП 16.13330.2017 Стальные конструкции;
-СП 339.1325800.2017 Конструкции из ячеистых бетонов;
-ГОСТ 31360-2007 Изделия стеновые неармированные из ячеистого бетона автоклавного твердения

2. В соответствии с "Техническим регламентом о безопасности зданий и сооружений" (ФЗ от 30.12.2009 №384-ФЗ):
- Степень огнестойкости здания - I
- Класс конструктивной пожарной опасности: С0.
- Класс ответственности здания: II (нормальный).
3. За отметку ±0,000 принята отметка чистого пола первого этажа, что соответствует абсолютной отметке 169,60.
4. Основные характеристики района строительства

Территория проектируемого объекта располагается на участке, отведенном в соответствии с ГПЗУ № РФ-77-4-53-3-25-2023-3232_ от 15.05.2023 г.. в г. Москва, внутригородское муниципальное образование Раменки.

Площадь территории составляет 4541 +24 кв. м.

Территория участка ограничена:
- с северо-восточной стороны – территорией городской поликлиники №209;
- с юго-восточной стороны – территорией посольства КНР;
- с северо-западной и юго-западной сторон – территорией сложившейся жилой застройки.
5. Основные характеристики здания:
- Расчетный срок службы здания II (не менее 50 лет);

Класс функциональной опасности:
- жилая часть – Ф1.3;
- нежилые помещения для коммерческого использования и нежилые помещения объединенной диспетчерской службы – Ф4.3;
- технические помещения – Ф5.1;
- помещения хозяйственных кладовых и хранения машин – Ф5.2.

Предусмотрено деление Объекта на следующие пожарные отсеки (ПО):
- подземная часть (автостоянка), включая кладовые и технические помещения;
- надземная часть.

Общие указания

1. Для контроля качества строительно-монтажных работ при строительстве генподрядчиком следует предоставить акты на скрытые работы, в том числе:
- монтаж перегородок;
- устройство всех видов гидроизоляций;
- устройство отделочных слоев под финишную отделку.

Акты на скрытые работы составлять в соответствии с требованиями СП 48.13330.2019 "Организация строительства" СНиП 12-01-2004 (с Изменением N 1).
2. Строительные работы в зимних условиях должны производиться с соблюдением требований соответствующих разделов: СП 70.13330.2012 Несущие и ограждающие конструкции. Актуализированная редакция СНиП 3.03.01-87 (с Изменением №1,3) СП 71.13330.2017 Изоляционные и отделочные покрытия. Актуализированная редакция СНиП 3.04.01-87 СП 12-135-2003 Безопасность труда в строительстве. Отраслевые типовые инструкции по охране труда Строительно-монтажные работы при среднесуточной температуре +5°С и минимальной суточной температуре ниже 0°С, а также при оттепелях производить в соответствии с "Указаниями по производству работ в зимних условиях",
разработанными в составе ППР технологических схемах на выполнение отдельных видов работ.
3. Внутренние стены выполнены из газобетонных блоков D600 (согласно СП 50.13330.2012, прил.Т.1, п.171) на клеевом составе: Y = 600 кг/м3 , d =250 мм, толщина кладки 250 мм; Y = 600 кг/м3 , d =200 мм, толщина кладки 200 мм; Y = 600 кг/м3 , d =150 мм, толщина кладки 150 мм; Y = 600 кг/м3 , d =100 мм, толщина кладки 100 мм, Y = 600 кг/м3 , d =80 мм, толщина кладки 80 мм. Наружные стены выполнить из блоков газобетонных автоклавного твердения Y500 кг/м3 , d =200мм. Наружные стены шахт ограждающих инженерные стояки выполнены из полнотелого кирпича КР-р-по 250х120х65/1НФ/150/2,0/50 толщиной 250мм
4. Кладку шахт ограждающих инженерные стояки выполнять после прокладки в них всех инженерных коммуникаций.
5. На кладочных чертежах слой штукатурки условно не показан. Размеры и привязки стен даны по поверхностям стен без учета отделки.
6. Все металлические элементы перемычек должны быть очищены от ржавчины и загрязнений, и окрашены пентафталевой эмалью ПФ-115 (ГОСТ 6465-2023) за два раза по грунту ГФ-021 (ГОСТ 25129-2020).
7. Устройство чистого пола выполнить после завершения работ по монтажу и испытанию инженерного оборудования.
8. После прокладки инженерных коммуникаций в перекрытиях и стенах необходимо восстановить предел огнестойкости, пространство вокруг коммуникаций заполнить негорючей базальтовой теплоизоляцией около кладочного материала и зачеканить цементно-песчаным раствором на всю толщину перекрытия и стен, обеспечивая нормируемый предел огнестойкости пересекаемых конструкций.
9. Сварные соединения выполнять по ГОСТ 5264-80. Ручную сварку производить электродами типа Э46А по ГОСТ 9467-75*. Катет сварного шва принимать по наименьшей толщине свариваемых элементов. Произвести визуальный и измерительный контроль (ВИК), перед этим сварные швы и смежные поверхности очистить от шлаков и металлических брызг. Данный метод применять на всех сварных соединениях производимых на площадки строительства. На особо ответственных участках несущих конструкций, по усмотрению заказчика применить один из дополнительных методов на выбор:
- магнитно-порошковый;
-ультразвуковой неразрушающий;
-тепловой;
-акустико-эмиссионный;
-радиографический;
-электрический.
10. Расположение инженерных сетей и оборудования см. рабочую документацию по инженерным системам здания.
11. Планировочные отметки земли уточнить по чертежам марки ГП.
12. Остальные указания см. на листах данного комплекта чертежей.

0.000 = +169.600

Изм.	Кол.уч.	Лист	№ док.	Подпись	Дата
1	1	Изм.	2032/25		07.2025
Разработал		Исаева			09.2024
Проверил		Суров			09.2024
ГАП		Захаров			09.2024
ГИП		Якубовский			09.2024
Н. контроль		Локтева			09.2024

133/23-ГК- АР6

«Жилой комплекс, расположенный по адресу: г. Москва, Мосфильмовская ул., вл. 31А, размещаемый на земельном участке, кадастровый № 77:07:0010004:24 (адресный ориентир: г.Москва, Мосфильмовская ул., вл.31А)»

Архитектурные решения. Лестничные клетки. Ограждения лестничных клеток

Стадия	Лист	Листов
РД	1	4

Общие данные

ОЛИМПРОЕКТ Архитектура. Изыскания. Проектирование.

Согласовано

Взам. инв. №

Подп. и дата

Инв. № подл.

Формат А2

Сечение Л7-Л7 (1 : 50)

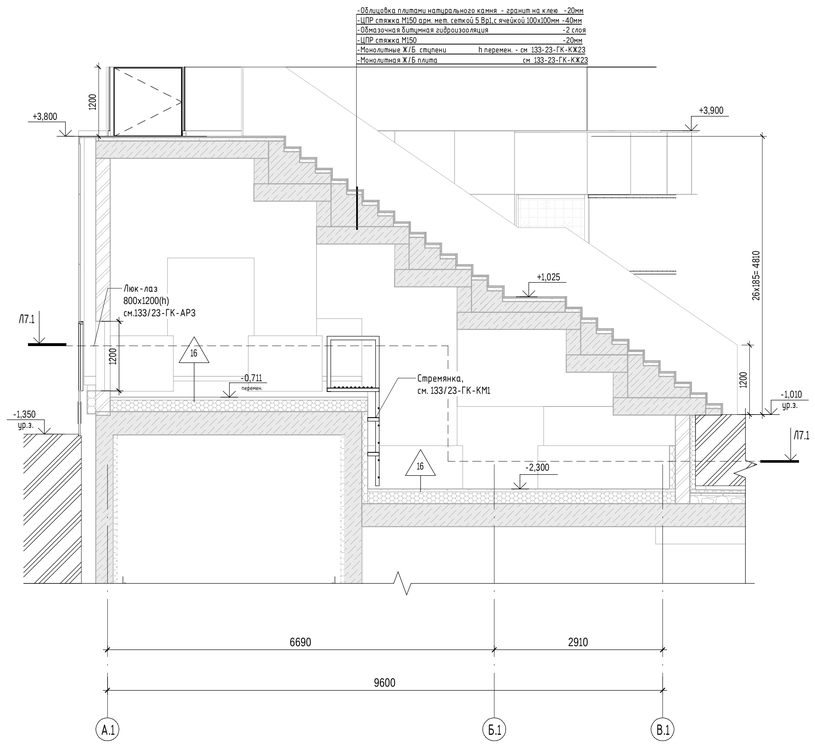

Лестница Л-7. План. (1 : 50)

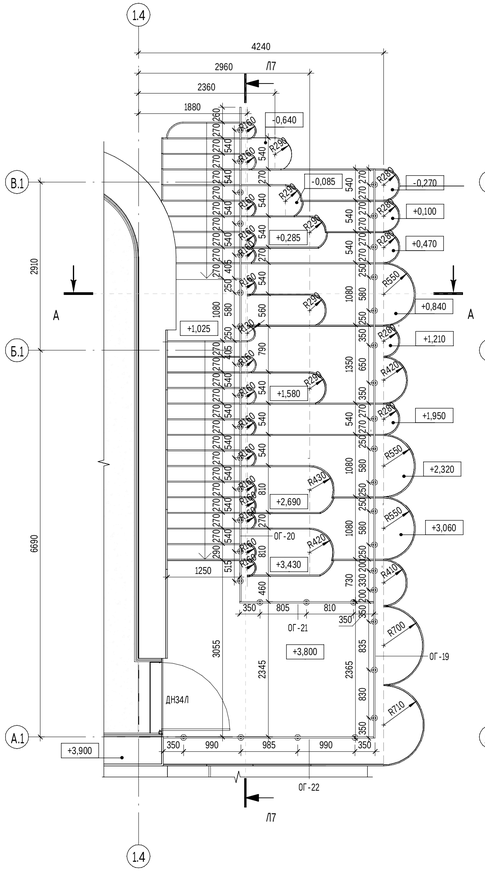

Сечение Л7.1 (1 : 50)

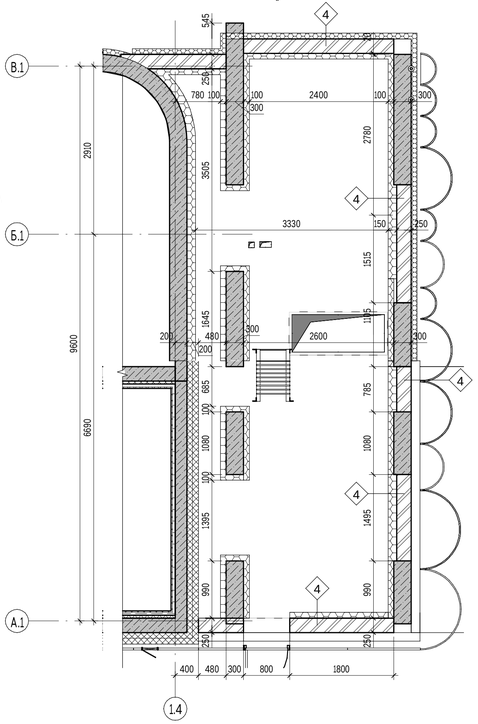

А-А. Узел облицовки ступеней (1 : 25)

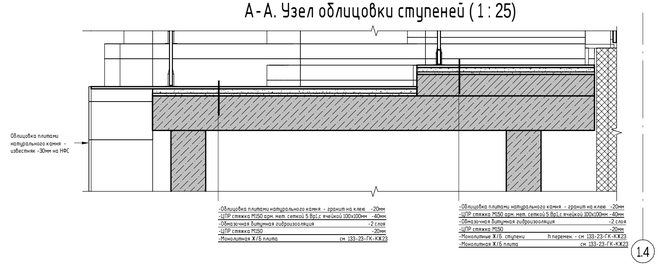

Спецификация элементов фасада. Строение 1. Лестница

Поз.	Наименование элементов фасада	Наименование материала отделки	Наименование и номер эталона цвета или образец колера	Ед. изм.	Примечание
Строение 1					
Фпод.п-1	Стены вертикальные плоские	Облицовочный натуральный камень (гранит), t=20мм	RAL 9001	10,5 м²	На клею
Фпод.р-1.1	Стены вертикальные по радиусу	Облицовочный натуральный камень (гранит), t=20мм	RAL 9001	1,3 м²	На клею
Фпод.п-2	Стены вертикальные плоские	Облицовочный натуральный камень (гранит), t=30мм	RAL 9001	0,8 м²	На клею
Фпод.р-2.1	Стены вертикальные по радиусу	Облицовочный натуральный камень (гранит), t=30мм	RAL 9001	0,2 м²	На клею
Фпод.п-3	Стены вертикальные плоские	Облицовочный натуральный камень (гранит) под дерево, t=20мм	RAL - 8002	0,2 м²	На клею
Фпод.р-3.1	Стены вертикальные по радиусу	Облицовочный натуральный камень (гранит) под дерево, t=20мм	RAL - 8002	0,2 м²	На клею
Фр-1	Стены вертикальные по радиусу	Облицовочный натуральный камень (известняк), t=30мм	RAL 9001	48,5 м²	На НФС системе
Фр-1.1	Стены вертикальные по радиусу	Облицовочный натуральный камень (гранит), t=30мм	RAL 9001	5,3 м²	На НФС системе
Фпод.п-4	Стены вертикальные плоские	Облицовочный натуральный камень (гранит) под дерево, t=20мм	RAL - 8002	8,3 м²	На клею
Фпод.р-4.1	Стены вертикальные по радиусу	Облицовочный натуральный камень (гранит) под дерево, t=20мм	RAL - 8002	1,8 м²	На клею
Фр-1.2	Стены вертикальные по радиусу	Облицовочный натуральный камень (гранит) под дерево, t=20мм	RAL - 8002	2,7 м²	На НФС системе
Фст-1	Ступень горизонтальная	Облицовочный натуральный камень (гранит) под дерево, t=20мм	RAL 8002	44,6 м²	На клею

Сводная ведомость материалов раздела 133/23-ГК-АР6

№ п/п	Обозначение	Наименование	Объем, м3	Примечание
4	ГОСТ530-2012	Кирпич полнотелый КР-р-по 250х120х65/1НФ/150/2,0/50 (t=250мм)	7,13	Армируется ВР сеткой через 5 рядов см. ППР
4.1	ГОСТ 28013-98	ЦПР стяжка М150 арм. мет. сеткой 5 Вр1, с ячейкой 100х100 мм - 60 мм	2,39	Армируется ВР сеткой см. ППР

Условные обозначения:

- Монолитные ж.б. конструкции
- Кирпич полнотелый КР-р-по 250х120х65/1НФ/150/2,0/50 (t=250мм)
- Утеплитель минераловатный плитный 1-й слой -1200х600х100, BASWOOL Лайт 35 (или аналог) λБ=0,041 Вт/м°К, ρ= 35кг/м³, W<0.5%, 100мм, 2-й слой -1200х600х100, BASWOOL ВЕНТ ФАСАД 80 (или аналог) прочность на сжатие при 10% линейной деформации не менее 0,015 МП
- Утеплитель плиты из пеностекла (ИЗОСТЕК) не менее ρ=130 кг/м³, предел прочности на сжатие ≥0,7 Мпа, λБ= 0,051 Вт/м°С, 100мм
- Утеплитель плиты из пеностекла (ИЗОСТЕК) не менее ρ=130 кг/м³, предел прочности на сжатие ≥0,7 Мпа, λБ= 0,051 Вт/м°С, 150мм
- Утеплитель плитный 1200х580х100, XPS ТЕХНОНИКОЛЬ CARBON PROF 300 (или аналог) прочность на сжатие при 10% линейной деформации не менее 0,2 МПа λ=0,032 Вт/м°С, W<0.2%, 100мм. Высотой -1800мм от ур. планировочного покрытия ГП
- Конструкция навесной фасадной системы с воздушным зазором с облицовкой плитами натурального камня/стеклофибробетона

+5,700 - Отметка чистого пола

ДВ1 EIWS60 - Марка заполнения дверного проема/ Огнестойкость

Л-1, Р-1 - Марка заполнения лючков и решеток

1 - Марка пола

- Отверстие в вертикальных конструкциях

Примечание:
1. Ограждения на эвакуационных лестничных клетках не должны заужать ширину площадки, ширину марша и просвет между маршами.
2. Схемы ограждений показаны условно и отображают принципиальный способ крепления. Крепление ограждений выполнять по технологии и узлам фирмы-производителя.
3. Спецификацию ограждений и узлы крепления см. лист 4 данного комплекта.
6. Площадь покрытия втирмной мастики ТЕХНОНИКОЛЬ MASTER 65м²
7. Детализацию фасадов см. 133/23-ГК-АР8, детализацию витражей см. 33/23-ГК-АР9.
8. Спецификацию элементов внутрилестничного пространства см. л. 10 123/33-ГК-АР4.
9. Перед заказом и монтажом отделочных элементов выполнить натурные обмеры геометрии наружной лестницы

0.000 = +169.600

Изм.	Кол.уч.	Лист	№ док.	Подпись	Дата
1	-	Зам.	2032/25		07.2025
Разработал		Исаева			07.2025
Проверил		Суров			07.2025
ГАП		Захаров			07.2025
ГИП		Якубовский			07.2025
Н. контроль		Локтева			07.2025

133/23-ГК- АР6

«Жилой комплекс, расположенный по адресу г. Москва, Мосфильмовская ул., вл. 31А, размещаемый на земельном участке, кадастровый № 77:07:0010004:24 (адресный ориентир: г.Москва, Мосфильмовская ул., вл.31А)»

Архитектурные решения. Лестничные клетки. Ограждения лестничных клеток

Стадия	Лист	Листов
РД	2	

Лестница Л-7

ОЛИМПРОЕКТ
Инженерно-Проектный Консалтинг

Согласовано

Взам. инв. №

Подп. и дата

Инв. № подл.

Формат А3х3

Л-1. Л8-Л8 (1 : 50)

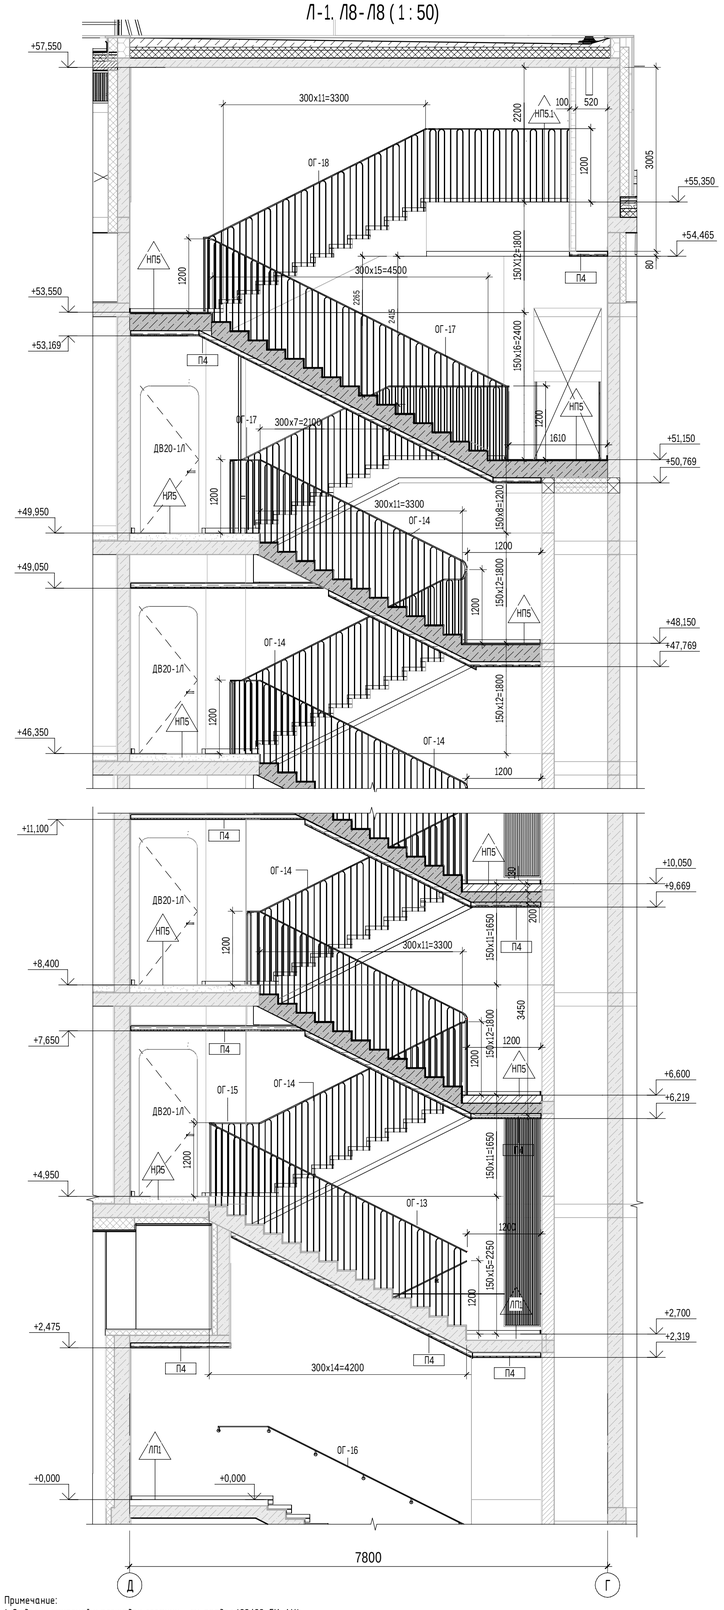

Л-1 на отм. +0,000 (1 : 50)

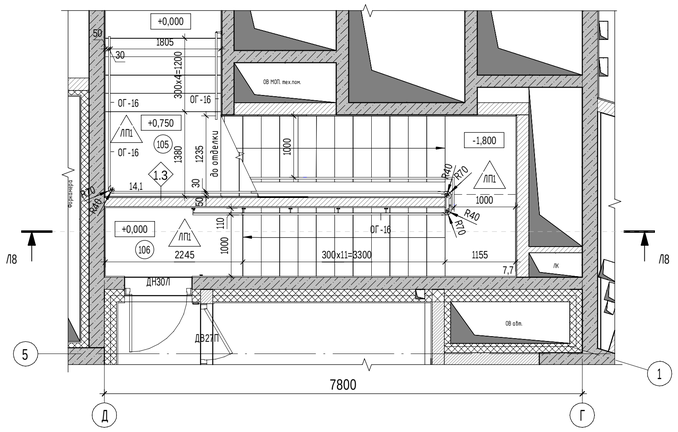

Л-1 на отм. +4.950 (1 : 50)

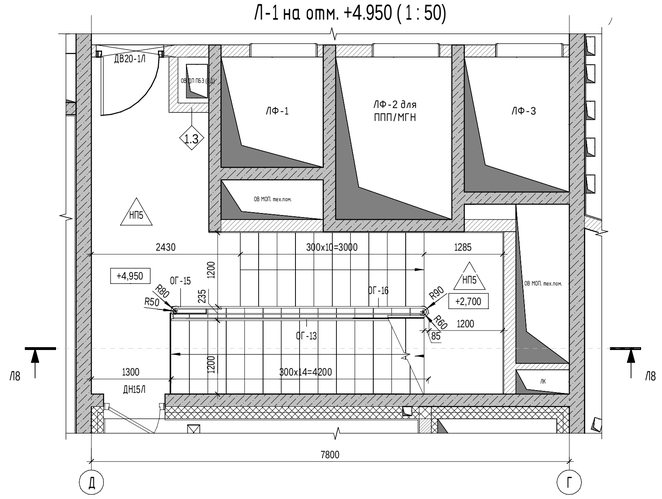

Л-1 на отм. +8.400 (1 : 50)

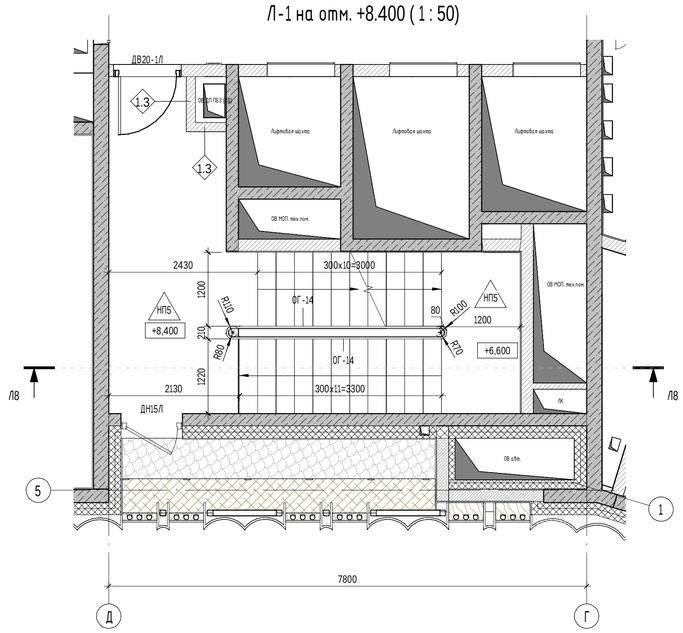

Л-1 на отм. +49,950 (1 : 50)

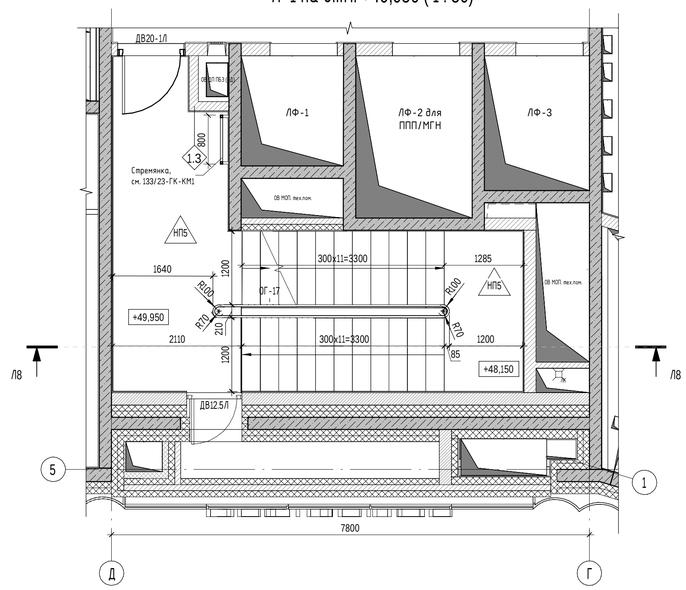

Л-1 на отм. +55.800 (1 : 50)

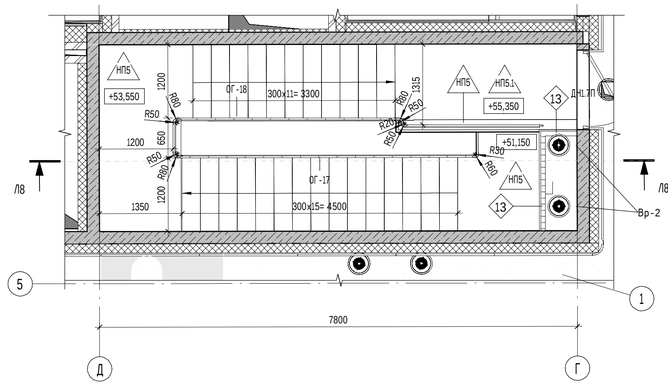

Ведомость материалов зашивок лестничной клетки Л-1

№ п/п	Обозначение	Наименование	Объем, м3	Примечание
13	ГОСТ Р 51829-2001	Зашивка на металлическом каркасе (КНАУФ-профиль ПН 75×40, КНАУФ-профиль ПС 75×50), 75мм; двухслойная обшивка КНАУФ-лист ГСП-А, 25мм – 100мм	0,65	

Условные обозначения:

- Конструкция навесной фасадной системы с воздушным зазором с облицовкой плитами натурального камня (толщ. 15-20 мм) – 50-400мм
- Монолитные ж.б. конструкции
- Блок газобетонный D600 (ГОСТ 31360-2024) В3,5: 600x200x250 - 200мм; 600x150x250 - 150мм; 600x100x250 - 100мм
- Утеплитель минераловатный плитный 1-й слой -1200x600x100, BASWOOL Лайт 35 (или аналог) λБ=0,041 Вт/м°К, ρ= 35кг/м³, W<0.5%, 100мм, 2-й слой -1200x600x100, ТЕХНОФАС ОПТИМА (или аналог) λБ = 0,044 Вт/м²°С, ρ= 120кг/м³, прочность при растяжении перпендикулярно лицевым поверхностям не менее 0,15 МП
- Утеплитель минераловатный плитный1200x600x100, ТЕХНОНИКОЛЬ ТЕХНОВЕНТ ОПТИМА (или аналог) прочность на сжатие при 10% линейной деформации не менее 0,012 МПа λБ=0,042 Вт/м°С, ρ= 90кг/м³, W<0.5%, 100мм
- ДВ1 - Марка заполнения дверного проема
- Покрытие просечно-вытяжное по балочной системе
- Марка покрытия
- Марка стены
- Инженерные отверстия
- +55,400 - Высотная отметка
- Воронка водоприемная кровельная
- Декоративный экран ниши радиатора отопления, см.раздел 133/23-ГК-АИ1

0.000 = +169.600

Примечание:
1. Отделку ступеней и площадок лестниц - см. раздел 133/23-ГК-АИ1.
2. Ограждения на эвакуационных лестничных клетках не должны заужать ширину площадки, ширину марша и просвет между маршами. Ширина прохода в свету для лестницы Л-1 выше отм. 0.000 равна 1200 мм "в свету".
3. Схемы ограждений показаны условно и отображают принципиальный способ крепления. Крепление ограждений выполнять по технологии и узлам фирмы-производителя.
4. Ограждение идёт непрерывно по всем этажам здания.
5. Спецификацию ограждения и узлы крепления см. лист 4 данного комплекта.
6. Доступ на тех.этаж осуществляется с 15 этажа по вертикальной лестнице из помещения МОП (лестничная клетка) через люк. см. 133/23-ГК-АР3 л.12-13, 16
7. Материал кладки и утеплителя см. раздел 133/23-ГК-АР4
8. Материал по фасаду см. раздел 133/23-ГК-АР8
9. Материал подшивки потолков, маршей и межмаршевых площадок см. 133/23-ГК-АИ1.

Согласовано

Взам. инв. №

Подп. и дата

Инв. № подл.

Изм.	Кол.уч.	Лист	№ док.	Подпись	Дата
1	-	Зам.	2032/25		07.2025

133/23-ГК- АР6

«Жилой комплекс, расположенный по адресу: г. Москва, Мосфильмовская ул., д.л. 31А, размещаемый на земельном участке, кадастровый № 77:07:0010004:24 (адресный ориентир: г.Москва, Мосфильмовская ул., д.л.31(А)»

Разработал	Исаева		09.2024
Проверил	Сыров		09.2024
ГАП	Захаров		09.2024
ГИП	Якубовский		09.2024
Н. контроль	Локтева		09.2024

Архитектурные решения. Лестничные клетки. Ограждения лестничных клеток

Стадия	Лист	Листов
РД	3	

Лестничная клетка Л-1. Надземная часть.

ОЛИМПРОЕКТ

Формат А1

ОГ-13 (1 : 50)

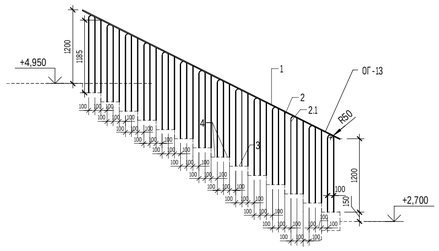

ОГ-14 (торцевой элемент) (1 : 50)

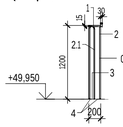

ОГ-14 (1 : 50)

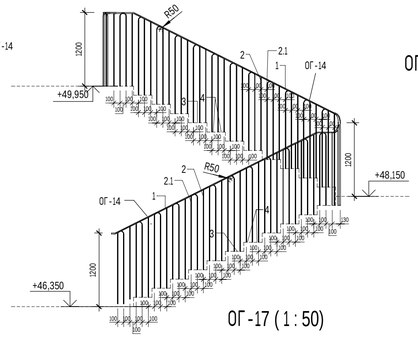

ОГ-14 (торцевой элемент) (1 : 50)

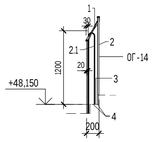

ОГ-16 (1 : 50)

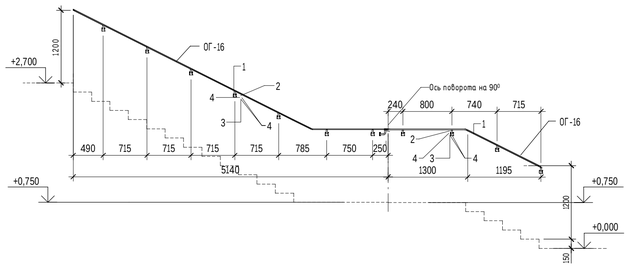

ОГ-17 (1 : 50)

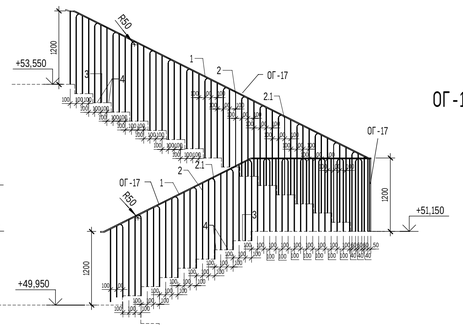

ОГ-17 (торцевой элемент) (1 : 50)

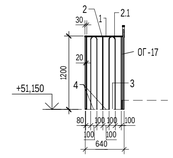

ОГ-18 (1 : 50)

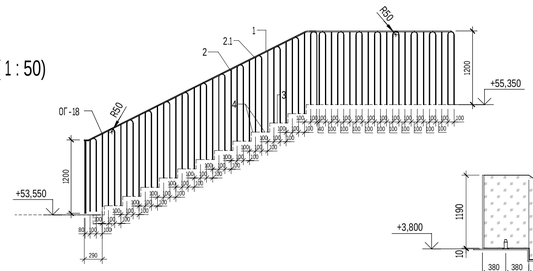

ОГ-18 (торцевой элемент) (1 : 50)

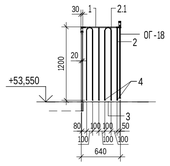

ОГ-20 (1 : 50)

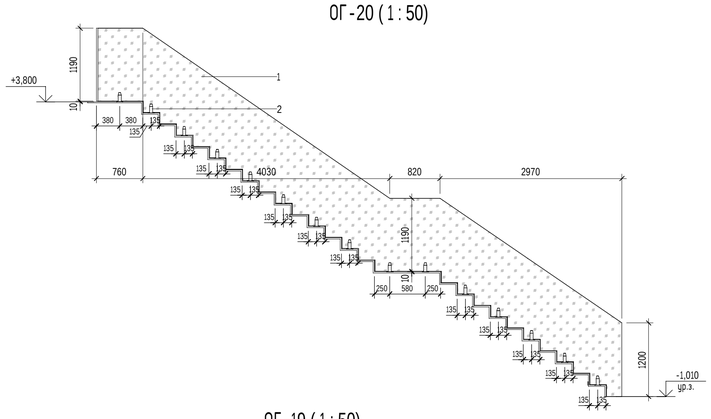

ОГ-15 (1 : 50)

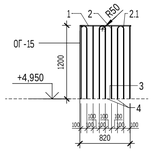

ОГ-16.1 (1 : 50)

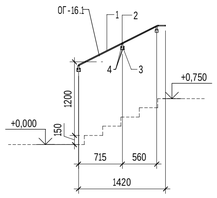

ОГ-19 (1 : 50)

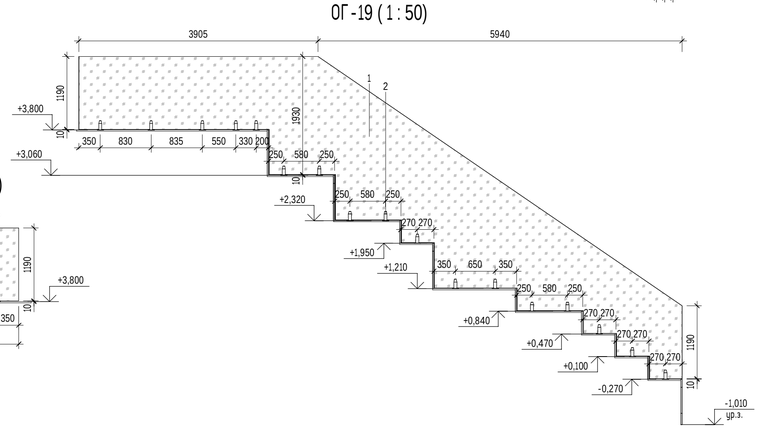

ОГ-22 (1 : 50)

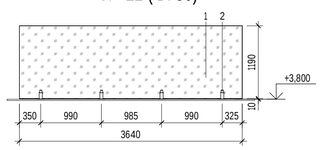

ОГ-21 (1 : 50)

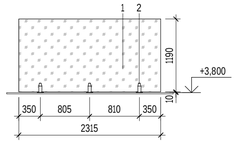

Примечание:
1. Решение по лестничным клеткам подземной части см. альбом 133/23-ГК-АР1, л. 7,8.
2. Уточненный узел крепления стеклянного ограждения см. технологические чертежи производителя изделия.
3 Закладные детали в монолитных лестницах см. раздел 133/23-ГК-КЖ18

Спецификация элементов ограждений НЧ

Поз.	Обозначение	Наименование	Кол.шт	Примечание
		ОГ-13, L=4 700	1	Крепление на ступень
1	ГОСТ 9941-81	Стальная труба 30х15х2 мм. Окраска в цвет металла Sunsong SNJS-22100, L=4 700	1	
2	ГОСТ 103-2006	Полоса стальная,прямая С245: 8х20 мм. Окраска в цвет металла Sunsong SNJS-22100. L= 1 185	13	
2.1	ГОСТ 103-2006	Полоса стальная П-образная гнутая С245:8х20. Окраска в цвет металла Sunsong SNJS-22100. L=2 450	14	
3	ГОСТ 103-76	Пластина стальная t=5мм 230х100	14	
4	ГОСТ Р 58387-2024,ГОСТ Р 57787-2017	Хим. анкер + анкер-шпилька 8х105мм	28	
		ОГ-14, L=8 910	13	Крепление на ступень
1	ГОСТ 9941-81	Стальная труба 30х15х2 мм. Окраска в цвет металла Sunsong SNJS-22100, L=8 910	1	
2	ГОСТ 103-2006	Полоса стальная, прямая С245: 8х20 мм. Окраска в цвет металла Sunsong SNJS-22100. L= 1 185	26	
2.1	ГОСТ 103-2006	Полоса стальная П-образная гнутая С245:8х20. Окраска в цвет металла Sunsong SNJS-22100. L=2 450	26	
3	ГОСТ 103-76	Пластина стальная t=5мм 230х100	27	
4	ГОСТ Р 58387-2024,ГОСТ Р 57787-2017	Хим. анкер + анкер-шпилька 8х105мм	54	
		ОГ-15, L=1 000	1	Крепление на ступень
1	ГОСТ 9941-81	Стальная труба 30х15х2 мм. Окраска в цвет металла Sunsong SNJS-22100, L=1 000	1	
2	ГОСТ 103-2006	Полоса стальная, прямая С245: 8х20 мм. Окраска в цвет металла Sunsong SNJS-22100. L= 1 185	3	
2.1	ГОСТ 103-2006	Полоса стальная П-образная гнутая С245:8х20. Окраска в цвет металла Sunsong SNJS-22100. L=2 450	3	
3	ГОСТ 103-76	Пластина стальная t=5мм 230х100	3	
4	ГОСТ Р 58387-2024,ГОСТ Р 57787-2017	Хим. анкер + анкер-шпилька 8х105мм	6	
		ОГ-16, L=8 590	1	Крепление к стене
1	ГОСТ 9941-81	Поручень металлический стальная труба 30х15мм.Окраска в цвет металла Sunsong SNJS-22100, L=8 590	1	
2	ГОСТ 9941-81	Гнутик стальной 70х70мм. Окраска в цвет металла Sunsong SNJS-22100	11	
3	ГОСТ 103-2006	Стальная пластина держателя поручня 50х50мм. Окраска в цвет металла Sunsong SNJS-22100	11	
4	Hilti HST M10x100	Анкер-шпилька Hilti HST M10x100	33	
		ОГ-16.1, L=1 410	1	Крепление к стене
1	ГОСТ 9941-81	Поручень металлический стальная труба 30х15мм.Окраска в цвет металла Sunsong SNJS-22100, L=1 410	1	
2	ГОСТ 9941-81	Гнутик стальной 70х70мм. Окраска в цвет металла Sunsong SNJS-22100	3	
3	ГОСТ 103-2006	Стальная пластина держателя поручня 50х50мм. Окраска в цвет металла Sunsong SNJS-22100	3	
4	Hilti HST M10x100	Анкер-шпилька Hilti HST M10x100	9	
		ОГ-17, L=10 685	1	Крепление на ступень
1	ГОСТ 9941-81	Стальная труба 30х15х2 мм. Окраска в цвет металла Sunsong SNJS-22100, L=10 685	1	
2	ГОСТ 103-2006	Полоса стальная, прямая С245: 8х20 мм. Окраска в цвет металла Sunsong SNJS-22100. L= 1 185	35	
2.1	ГОСТ 103-2006	Полоса стальная П-образная гнутая С245:8х20. Окраска в цвет металла Sunsong SNJS-22100. L=2 450	32	
3	ГОСТ 103-76	Пластина стальная t=5мм 230х100	31	
4	ГОСТ Р 58387-2024,ГОСТ Р 57787-2017	Хим. анкер + анкер-шпилька 8х105мм	62	
		ОГ-18, L=7 085	1	Крепление на ступень
1	ГОСТ 9941-81	Стальная труба 30х15х2 мм. Окраска в цвет металла Sunsong SNJS-22100, L=7 085	1	
2	ГОСТ 103-2006	Полоса стальная, прямая С245: 8х20 мм. Окраска в цвет металла Sunsong SNJS-22100. L= 1 185	22	
2.1	ГОСТ 103-2006	Полоса стальная П-образная гнутая С245:8х20. Окраска в цвет металла Sunsong SNJS-22100. L=2 450	23	
3	ГОСТ 103-76	Пластина стальная t=5мм 230х100	25	
4	ГОСТ Р 58387-2024,ГОСТ Р 57787-2017	Хим. анкер + анкер-шпилька 8х105мм	50	
		ОГ-19, L= 9 850	1	Крепление на ступень
1	ГОСТ Р 56926-2016	Стеклянное ограждение - триплекс 8зак-EVA-8зак 1190х10, L=9 850	1	
2	Индивидуальный	Крепление ограждения- министойки, h=190мм, d=89 мм, полированная нержавеющая сталь L=0	17	
		ОГ-20, L=8 560	1	Крепление на ступень
1	ГОСТ Р 56926-2016	Стеклянное ограждение - триплекс 8зак-EVA-8зак 1190х10, L=8 560	1	
2	Индивидуальный	Крепление ограждения- министойки, h=190мм, d=89 мм, полированная нержавеющая сталь L=0	15	
		ОГ-21, L=2 320	1	Крепление на ступень
1	ГОСТ Р 56926-2016	Стеклянное ограждение - триплекс 8зак-EVA-8зак 1190х10, L=2 320	1	
2	Индивидуальный	Крепление ограждения- министойки, h=190мм, d=89 мм, полированная нержавеющая сталь L=0	3	
		ОГ-22, L=3 640	1	Крепление на ступень
1	ГОСТ Р 56926-2016	Стеклянное ограждение - триплекс 8зак-EVA-8зак 1190х10, L=3 640	1	
2	Индивидуальный	Крепление ограждения- министойки, h=190мм, d=89 мм, полированная нержавеющая сталь L=0	4	

Ведомость ограждений лестниц

Поз.	Наименование	Описание	Длина	Примечание	Кол-во
ОГ-13	Инд. изготовления	Ограждение стальное .Окраска в цвет металла Sunsong SNJS-22100	4,7 м		1
ОГ-14	Инд. изготовления	Ограждение стальное .Окраска в цвет металла Sunsong SNJS-22100	107,2 м		13
ОГ-15	Инд. изготовления	Ограждение стальное .Окраска в цвет металла Sunsong SNJS-22100	1,0 м		1
ОГ-16	Инд. изготовления	Ограждение стальное .Окраска в цвет металла Sunsong SNJS-22100	10,2 м		2
ОГ-17	Инд. изготовления	Ограждение стальное .Окраска в цвет металла Sunsong SNJS-22100	10,7 м		1
ОГ-18	Инд. изготовления	Ограждение стальное .Окраска в цвет металла Sunsong SNJS-22100	7,1 м		1
ОГ-19	Инд.изготовление	Ограждение на лестнице из стекла триплекс 8зак-EVA-8зак	9,85 м		1
ОГ-20	Инд.изготовление	Ограждение на лестнице из стекла триплекс 8зак-EVA-8зак	8,56 м		1
ОГ-21	Инд.изготовление	Ограждение на лестнице из стекла триплекс 8зак-EVA-8зак	2,32 м		1
ОГ-22	Инд.изготовление	Ограждение на лестнице из стекла триплекс 8зак-EVA-8зак	3,64 м		1

Схема ограждения (ОГ-13, 14, 15, 17, 18)

А-А

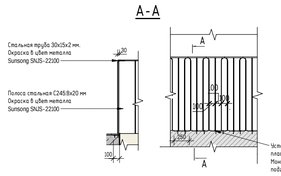

Схема крепления поручней- ОГ-16, 16.1

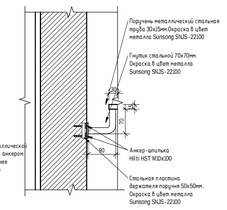

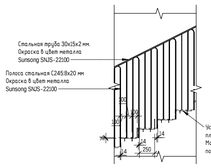

Схема крепления ограждения сверху марша (ОГ-19-22)

3d-вид крепление поручня на ступень (ОГ-13, 14, 15, 17, 18)

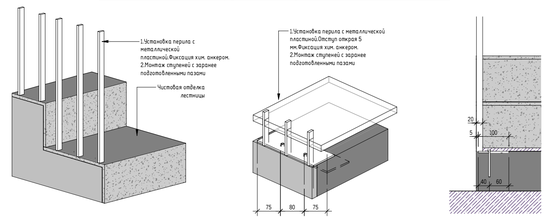

Примечания:

1. Общие цказания см. л. 1;
2. Все ограждения должны быть рассчитаны на восприятие горизонтальной нагрузки не менее 0,5кН.

0.000 = +169.600

Изм.	Кол.уч.	Лист	№ док.	Подпись	Дата
1	-	Зам.	2032/25		07.2025

Разработал	Исаева		09.2024
Проверил	Суров		09.2024
ГАП	Захаров		09.2024
ГИП	Якубовский		09.2024
Н. контроль	Локтева		09.2024

133/23-ГК- АР6

«Жилой комплекс, расположенный по адресу: г. Москва, Мосфильмовская ул., вл. 31А, размещаемый на земельном участке, кадастровый № 77:07:0010004:24 (адресный ориентир: г.Москва, Мосфильмовская ул., вл.31А)»

Архитектурные решения. Лестничные клетки. Ограждения лестничных клеток

Стадия	Лист	Листов
РД	4	

Ограждения

ОЛИМПРОЕКТ Архитектура. Инженерия. Проектирование

Согласовано

Взам. инв. №

Подп. и дата

Инв. № подл.

Формат А1